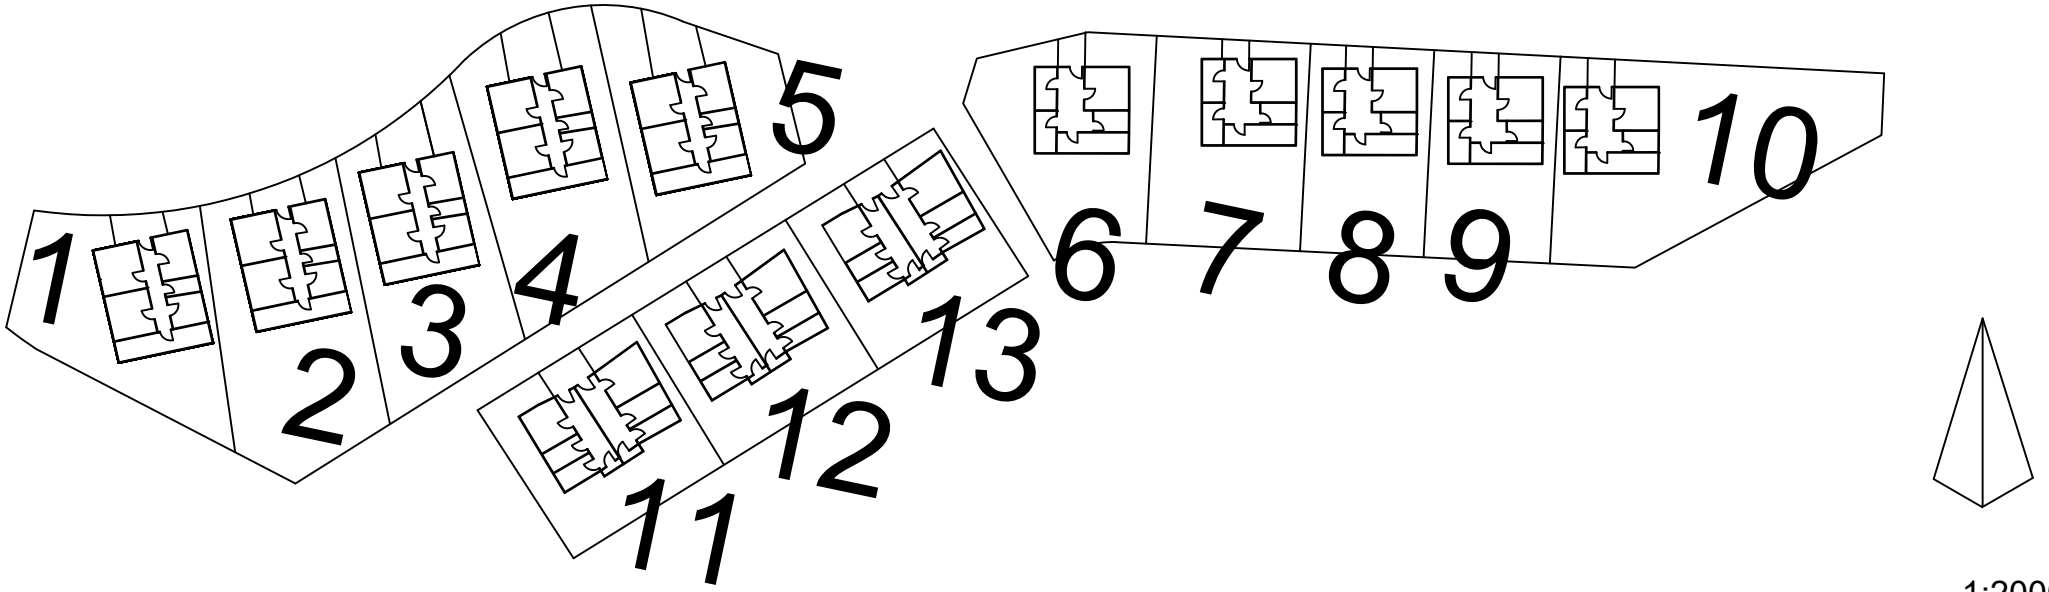

1:2000

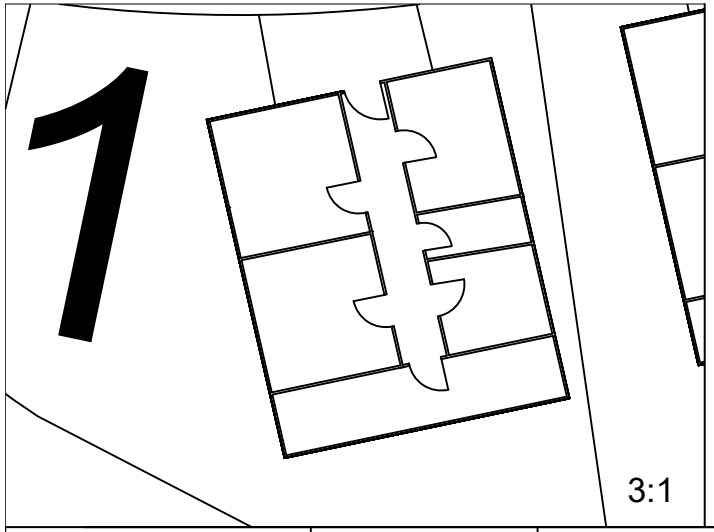

3:1

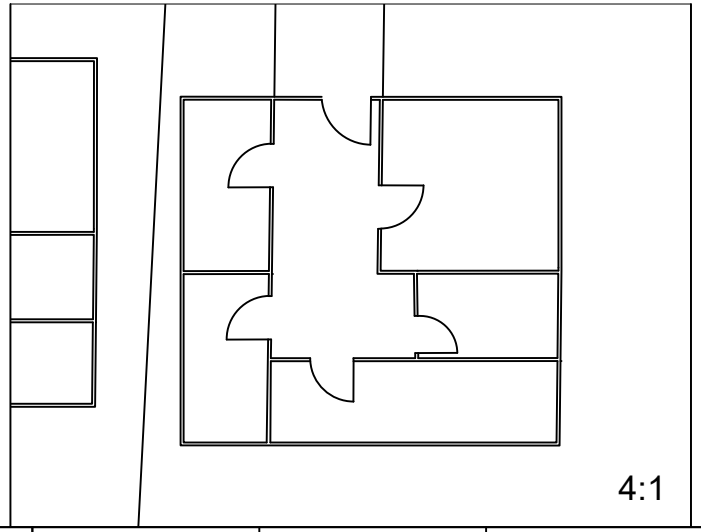

4:1

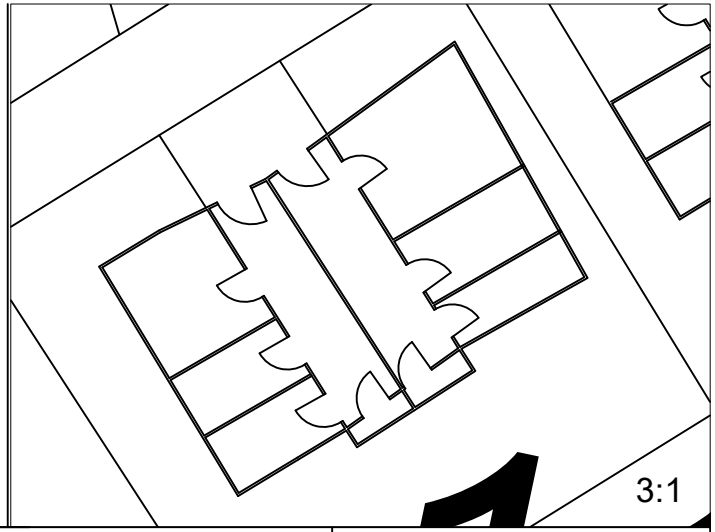

3:1

	Nombre	Fecha	Escala			Nº Plano: 01
Dibujado	F. Javier Ruiz	28/01/2021				Sustituye a:
Comprobado						Sustituido por: